


# OAKWOOD

## FLAT NO.- 4 COMMON TOILET

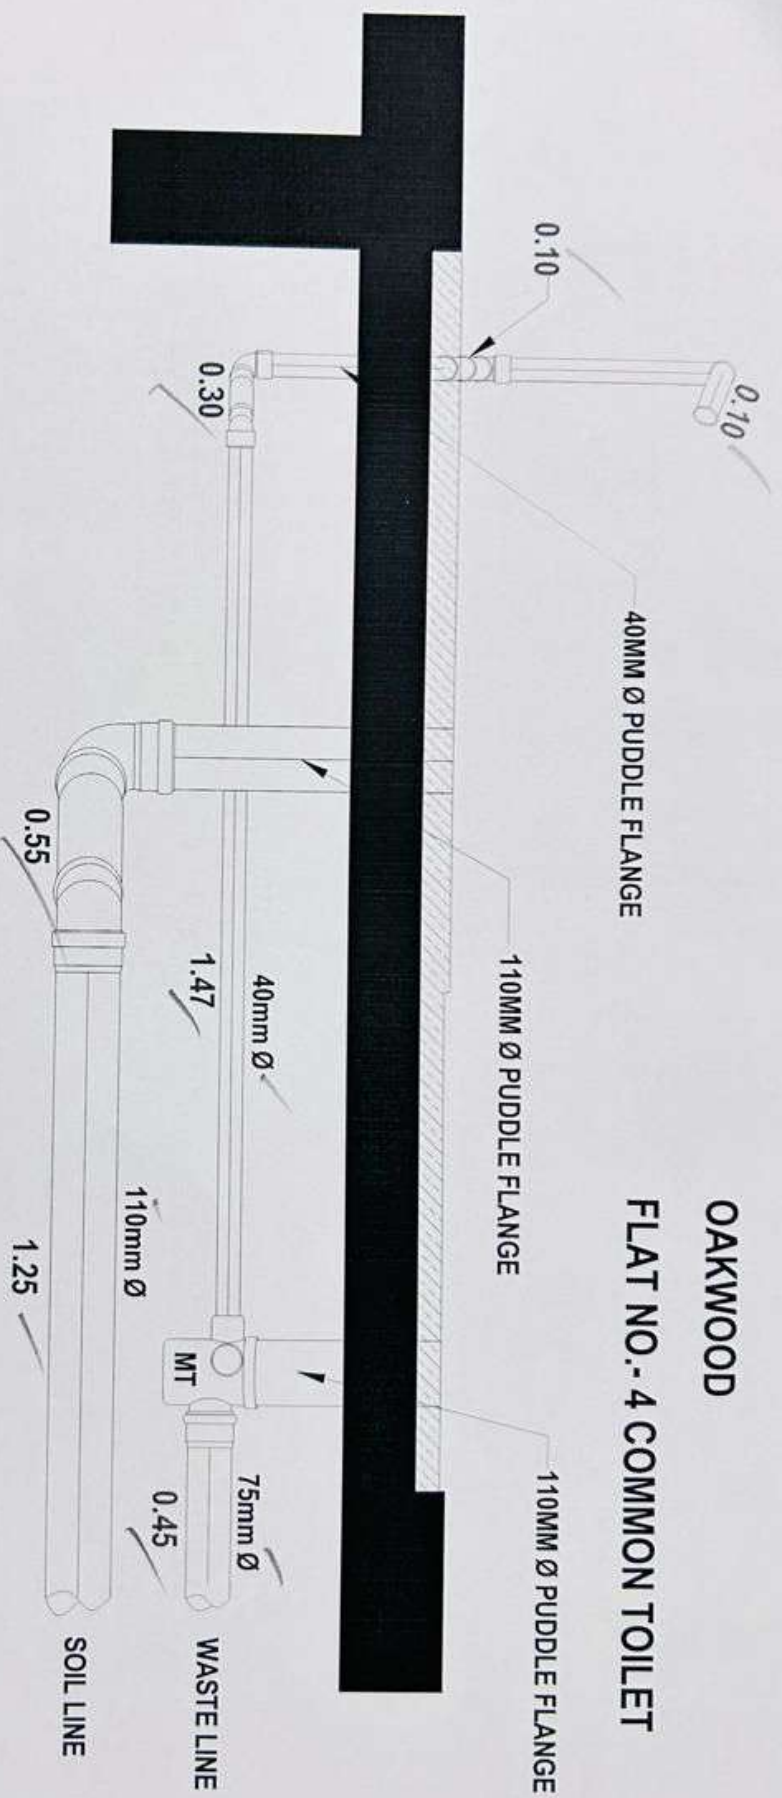


- 1- 110 MM Ø PVC SWR TYPE-B PIPE -  $1.25+0.55 = 1.80$  MTR. ✓
- 2- 75 MM Ø PVC SWR TYPE-B PIPE - 0.45 MTR. ✓
- 3- 40 MM Ø AGRI. 6KG. PIPE -  $1.47+0.30+0.10+0.10 = 1.97$  MTR. ✓
- 4- 110X75X50 MM Ø MULTI TRAP - 1 NO. ✓
- 5- 110X600 MM Ø PVC PUDDLE FLANGE - 2 NOS. ✓
- 6- 40X800 MM Ø PVC PUDDLE FLANGE - 1 NO. ✓

157

80/12/25



# OAKWOOD FLAT NO.- 4 KITCHEN

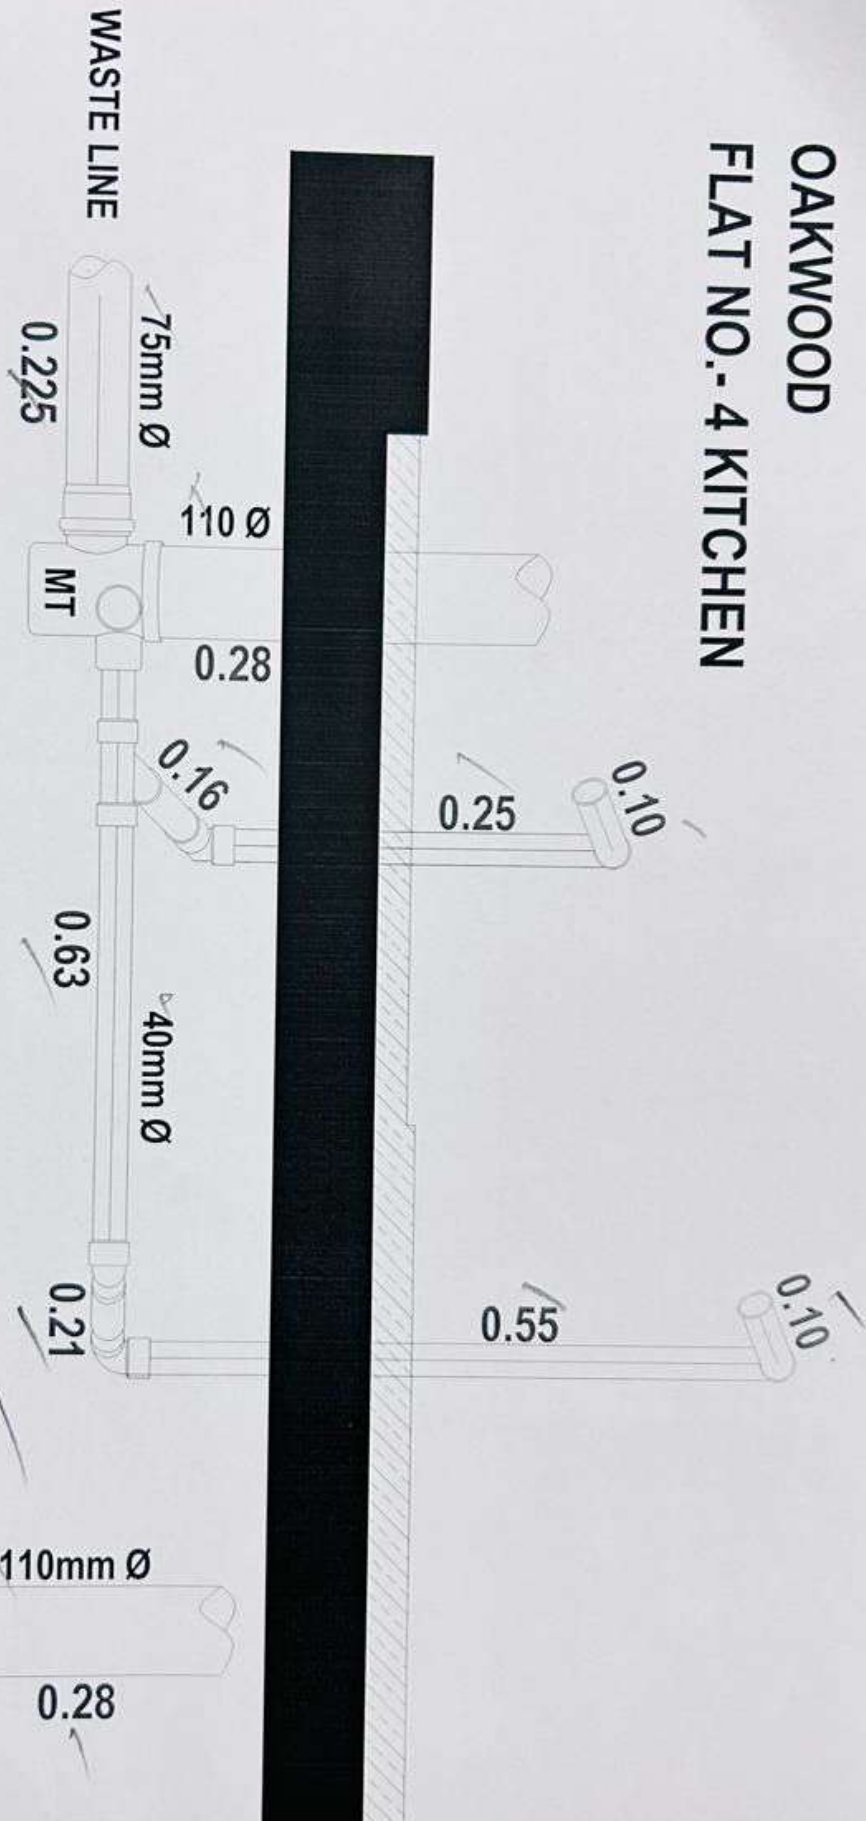


- 1- 110 MM Ø PVC SWR TYPE-B PIPE -  $0.28+0.28 = 0.56$  MTR. ✓
- 2- 75 MM Ø PVC SWR TYPE-B PIPE -  $0.225+0.20 = 0.425$  MTR. ✓
- 3- 40 MM Ø AGRI. 6KG. PIPE -  $0.10+0.55+0.21+0.63+0.16+0.25+0.10 = 2.00$  MTR. ✓
- 4- 110X75X50 MM Ø MULTI TRAP - 1 NO. ✓
- 5- 110X75 MM Ø FLOOR TRAP - 1 NO. ✓

*Handwritten signature and date:*  
20/12/25



FLAT NO.-3 MASTER TOILET

110MM Ø PUDDLE FLANGE

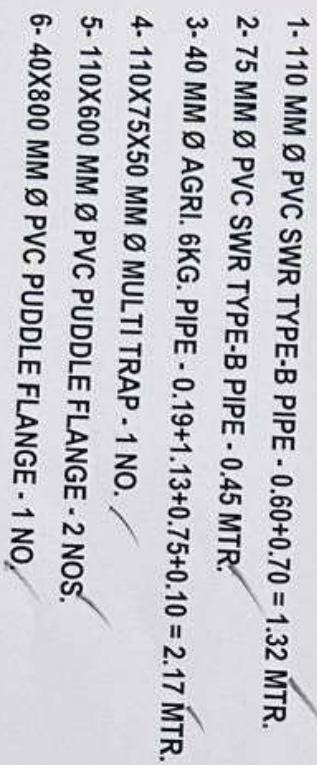


2nd  
307/12/25



# OAKWOOD

## FLAT NO.- 3 COMMON TOILET

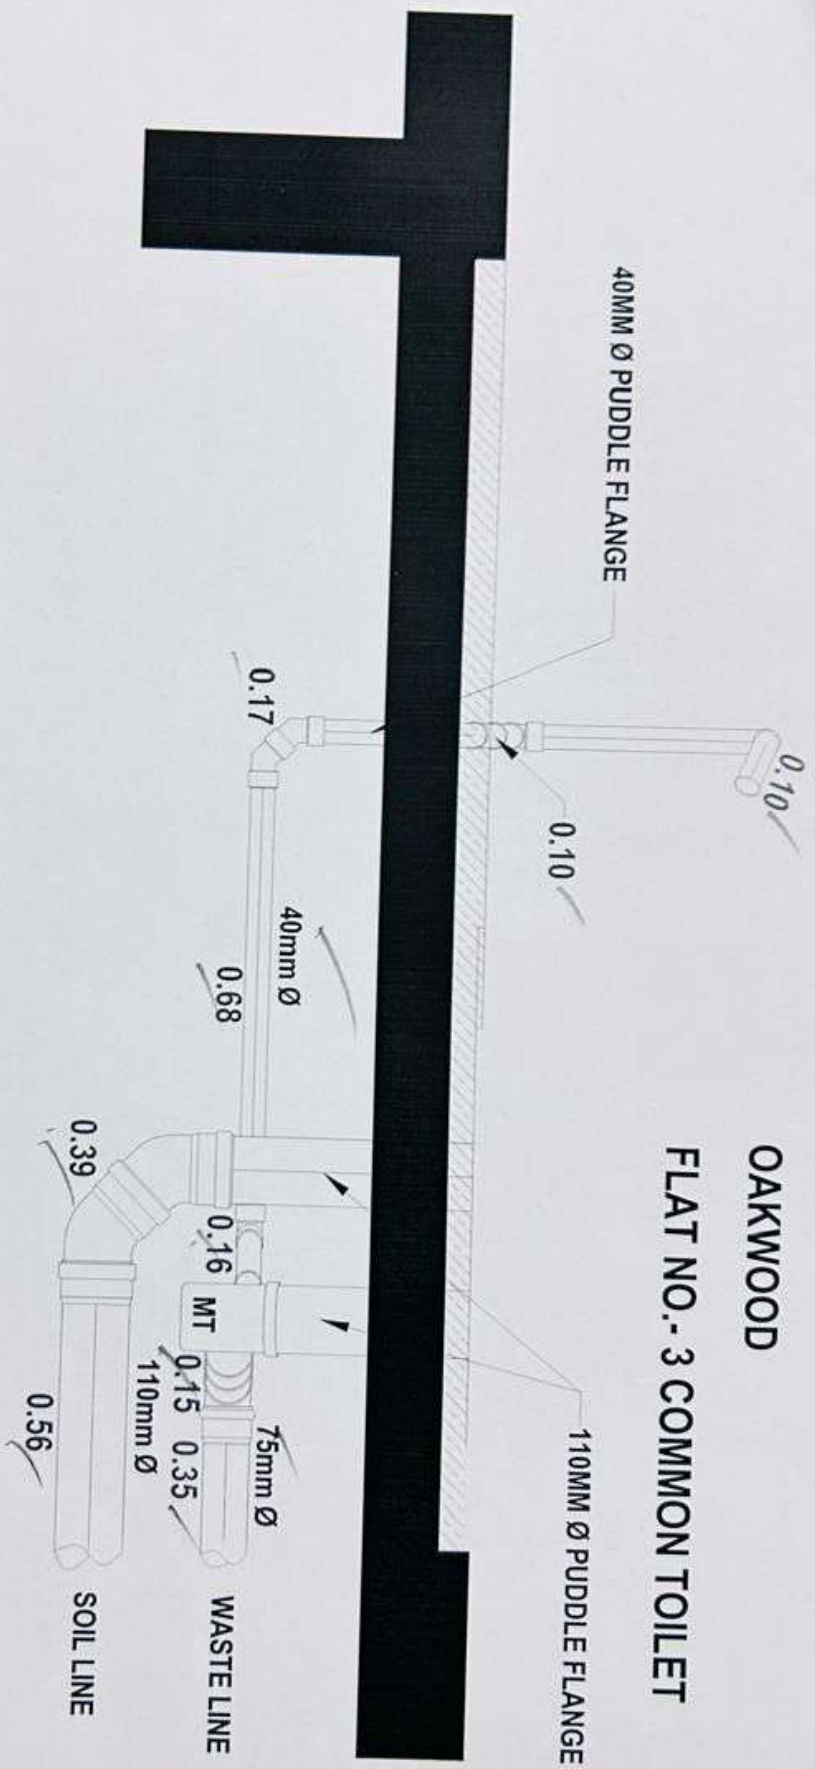


- 1- 110 MM Ø PVC SWR TYPE-B PIPE -  $0.39+0.56 = 0.95$  MTR. ✓
- 2- 75 MM Ø PVC SWR TYPE-B PIPE -  $0.15+0.35 = 0.50$  MTR. ✓
- 3- 40 MM Ø AGRI. 6KG. PIPE -  $0.16+0.68+0.17+0.10+0.10 = 1.21$  MTR. ✓
- 4- 110X75X50 MM Ø MULTI TRAP - 1 NO. ✓
- 5- 110X600 MM Ø PVC PUDDLE FLANGE - 2 NOS. ✓
- 6- 40X800 MM Ø PVC PUDDLE FLANGE - 1 NO. ✓

13/12/25  
30/12/25



# OAKWOOD FLAT NO.- 3 KITCHEN

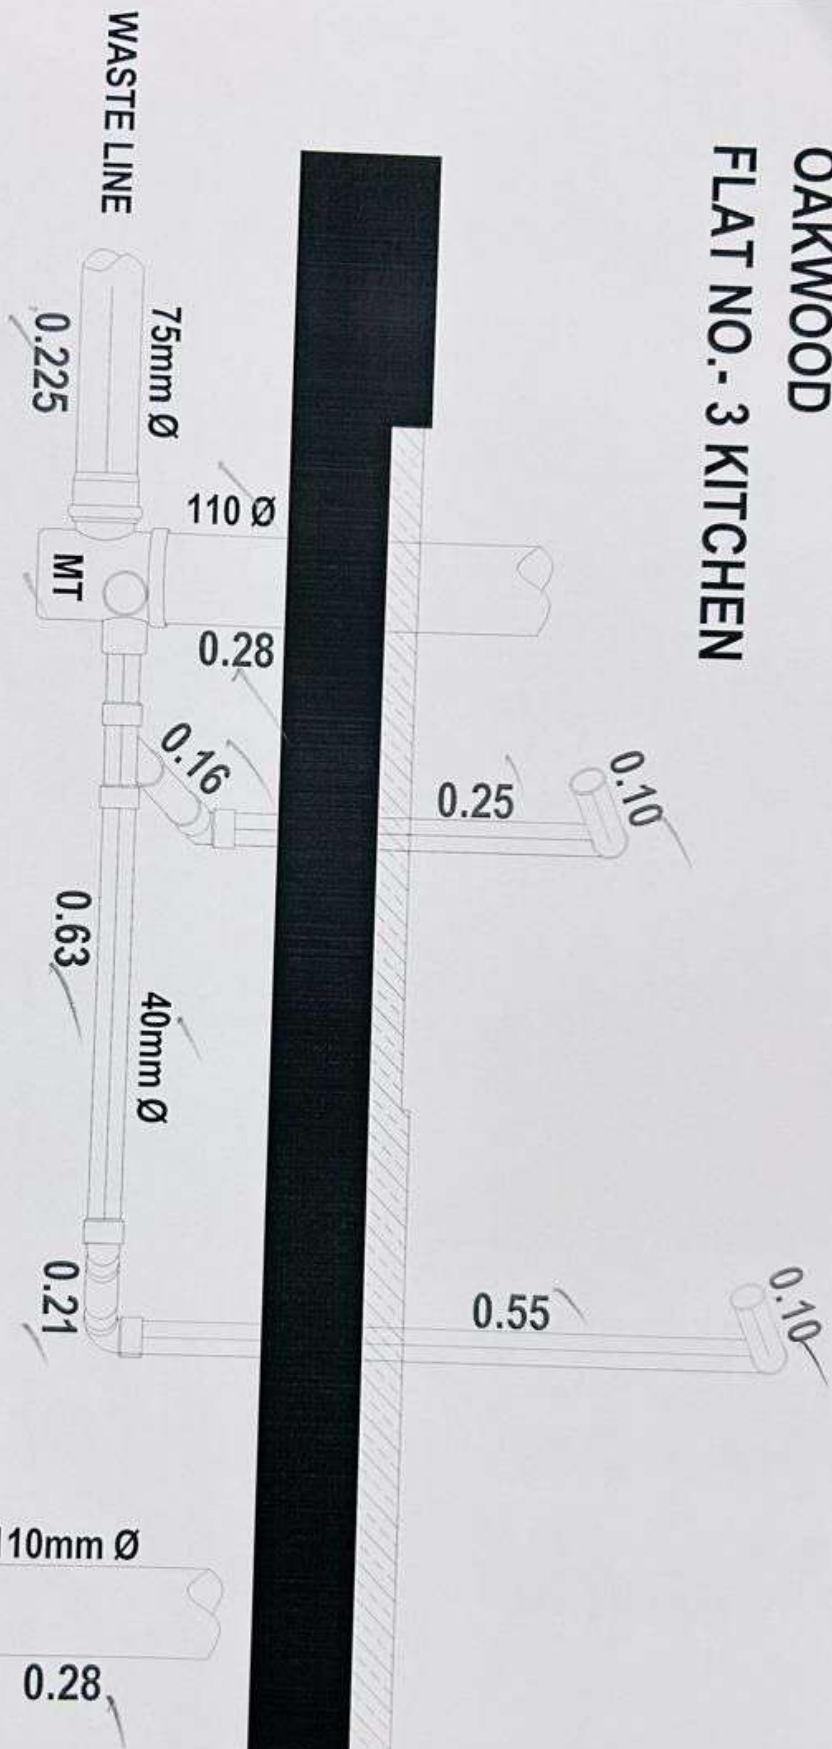

- 1- 110 MM Ø PVC SWR TYPE-B PIPE -  $0.28+0.28 = 0.56$  MTR.
- 2- 75 MM Ø PVC SWR TYPE-B PIPE -  $0.225+0.20 = 0.425$  MTR.
- 3- 40 MM Ø AGRI. 6KG. PIPE -  $0.10+0.55+0.21+0.63+0.16+0.25+0.10 = 2.00$  MTR.
- 4- 110X75X50 MM Ø MULTI TRAP - 1 NO.
- 5- 110X75 MM Ø FLOOR TRAP - 1 NO.


BALCONY

30/12/25



# OAKWOOD

## FLAT NO.-2 MASTER TOILET

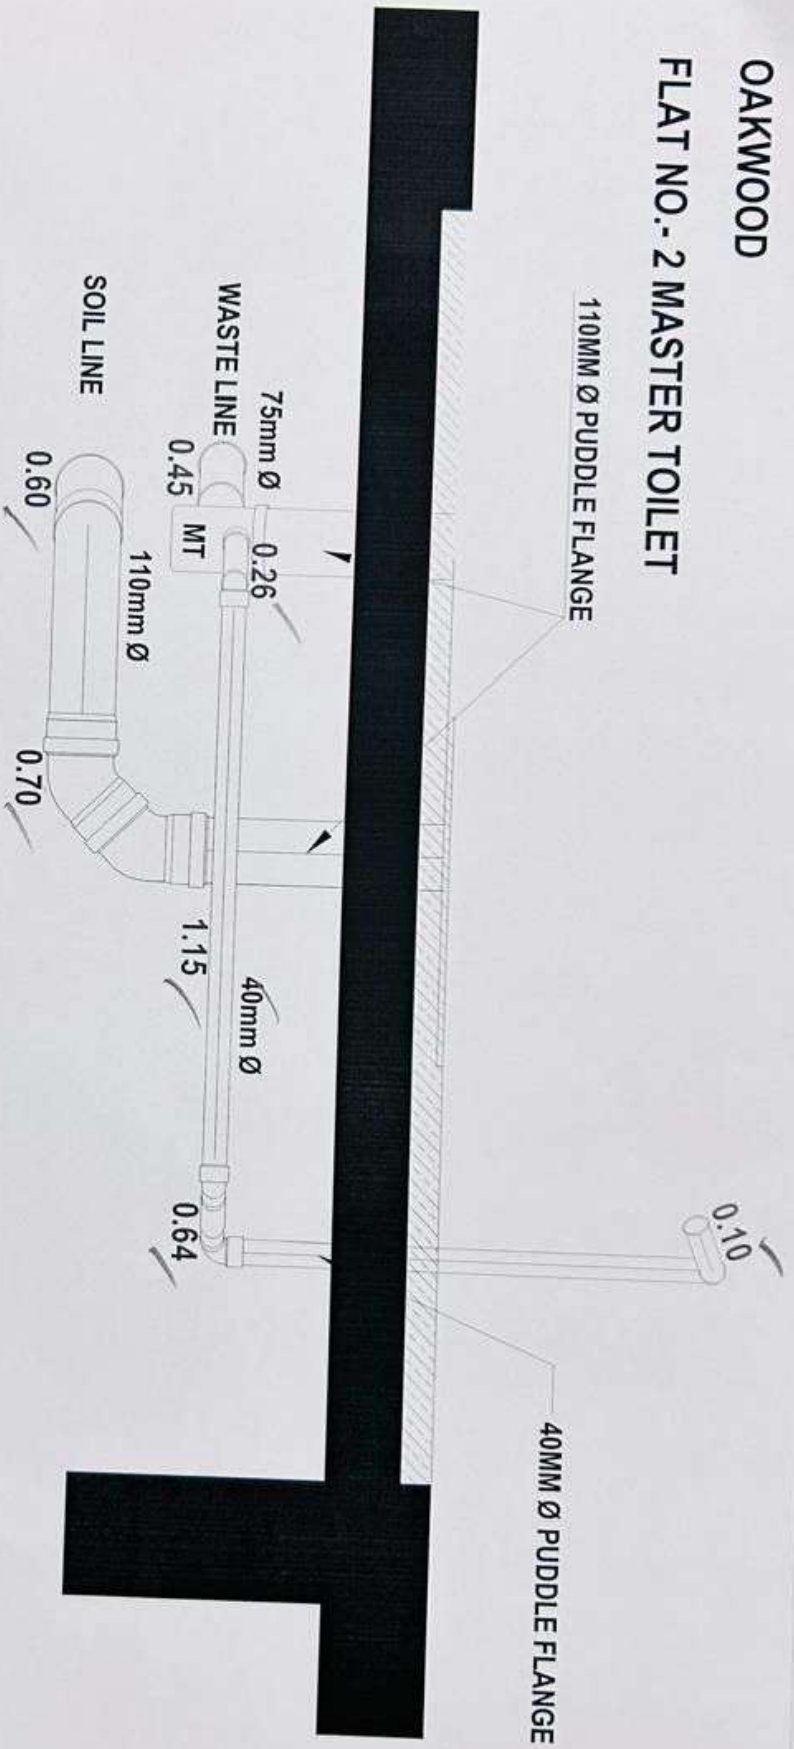


- 1- 110 MM Ø PVC SWR TYPE-B PIPE -  $0.60+0.70 = 1.30$  MTR. ✓
- 2- 75 MM Ø PVC SWR TYPE-B PIPE - 0.45 MTR. ✓
- 3- 40 MM Ø AGRI. 6KG. PIPE -  $0.26+1.15+0.64+0.10 = 2.15$  MTR. ✓
- 4- 110X75X50 MM Ø MULTI TRAP - 1 NO. ✓
- 5- 110X600 MM Ø PVC PUDDLE FLANGE - 2 NOS. ✓
- 6- 40X800 MM Ø PVC PUDDLE FLANGE - 1 NO. ✓

13/5  
20/12/25



# OAKWOOD

## FLAT NO.-2 COMMON TOILET

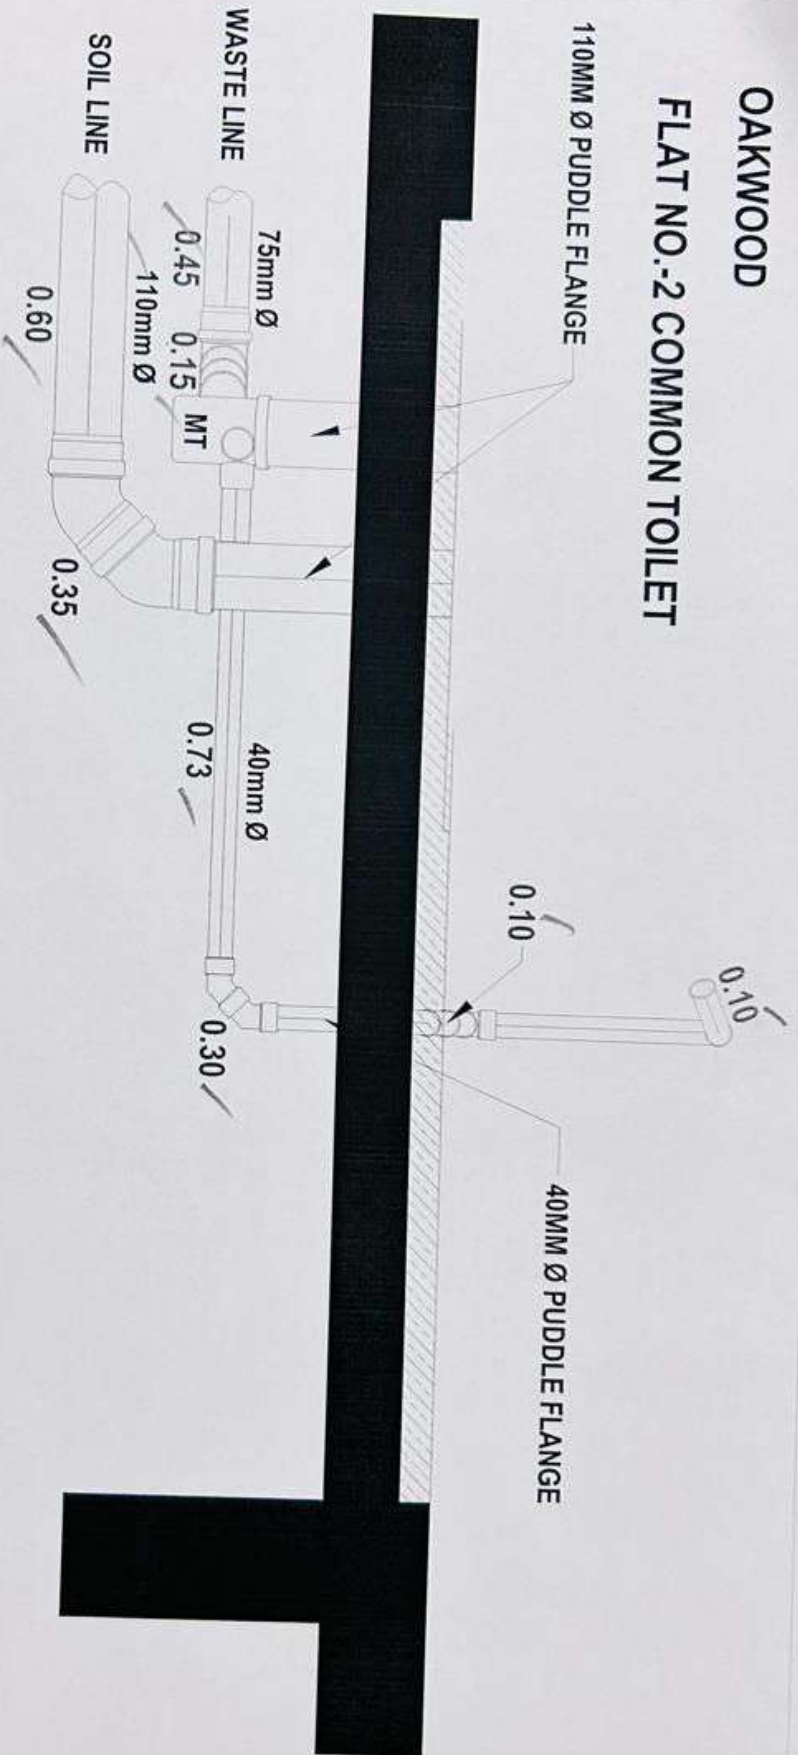


- 1- 110 MM Ø PVC SWR TYPE-B PIPE -  $0.60+0.35 = 0.95$  MTR.
- 2- 75 MM Ø PVC SWR TYPE-B PIPE -  $0.45+0.15 = 0.60$  MTR.
- 3- 40 MM Ø AGRI. 6KG. PIPE -  $0.73+0.30+0.10+0.10 = 1.23$  MTR.
- 4- 110X75X50 MM Ø MULTI TRAP - 1 NO.
- 5- 110X600 MM Ø PVC PUDDLE FLANGE - 2 NOS.
- 6- 40X800 MM Ø PVC PUDDLE FLANGE - 1 NO.

13/1


2nd  
30/12/25



# OAKWOOD FLAT NO.- 2 KITCHEN

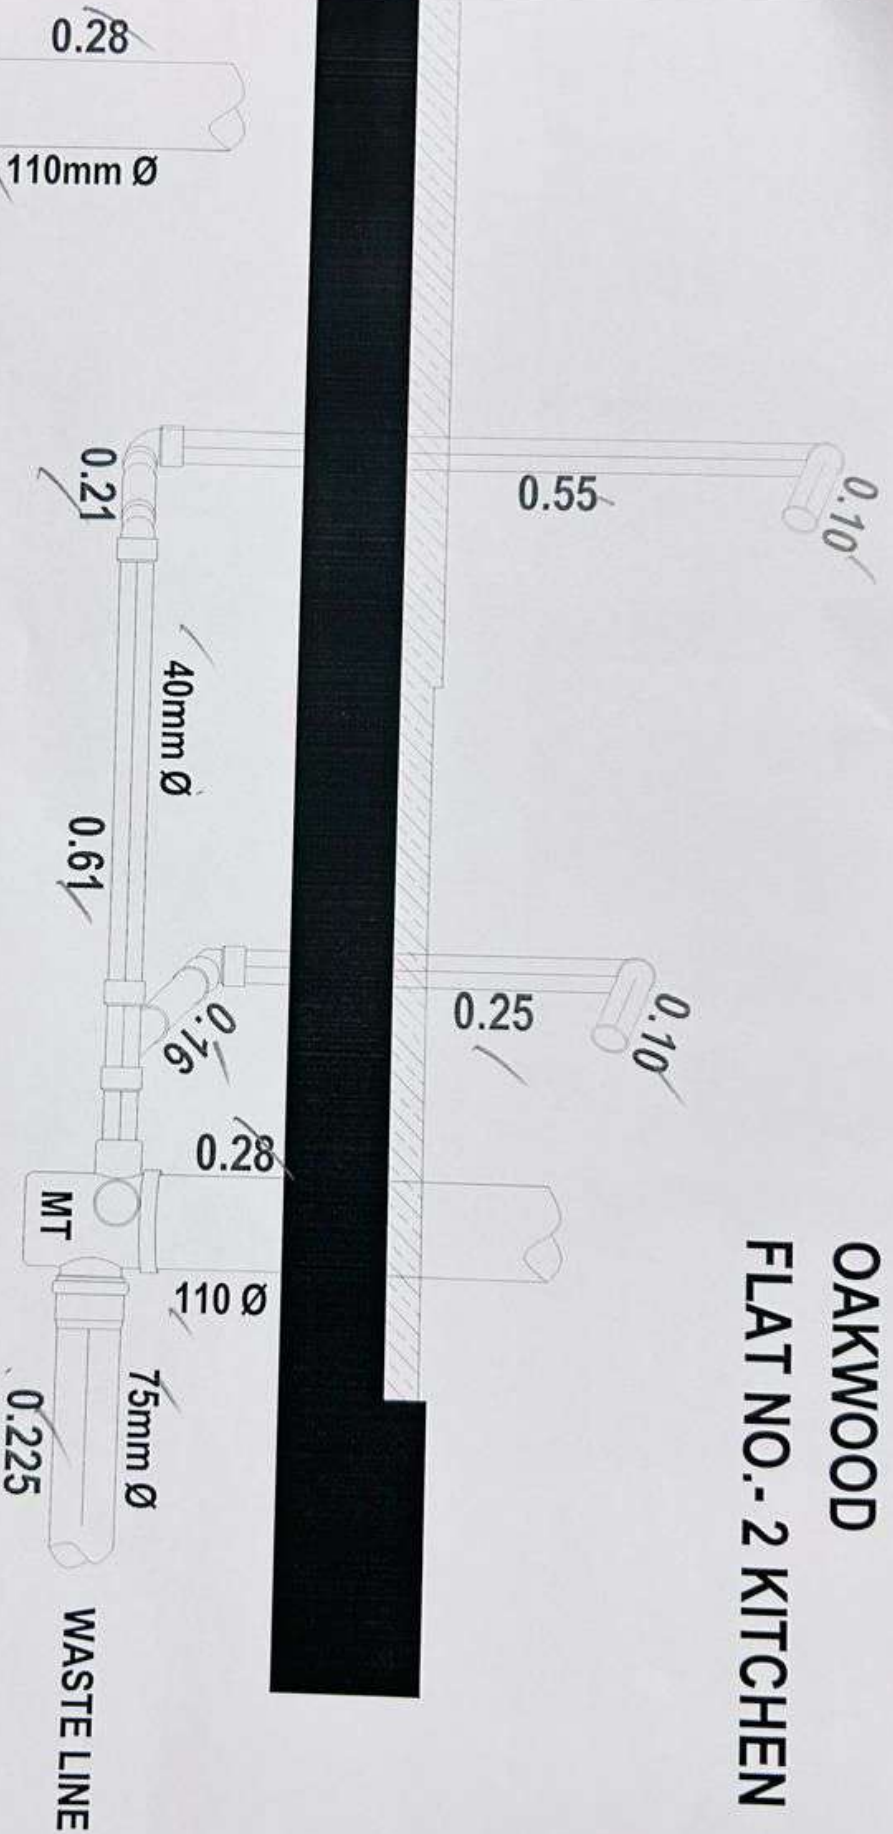

BALCONY

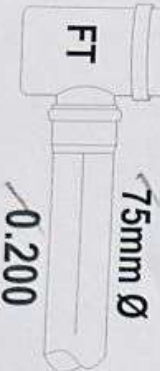

- 1- 110 MM Ø PVC SWR TYPE-B PIPE -  $0.28+0.28 = 0.56$  MTR.
- 2- 75 MM Ø PVC SWR TYPE-B PIPE -  $0.225+0.20 = 0.425$  MTR.
- 3- 40 MM Ø AGRI. 6KG. PIPE -  $0.10+0.55+0.21+0.61+0.16+0.25+0.10 = 1.98$  MTR.
- 4- 110X75X50 MM Ø MULTI TRAP - 1 NO.
- 5- 110X75 MM Ø FLOOR TRAP - 1 NO.


15/12/18

80712/18



# OAKWOOD

## FLAT NO.- 1 MASTER TOILET

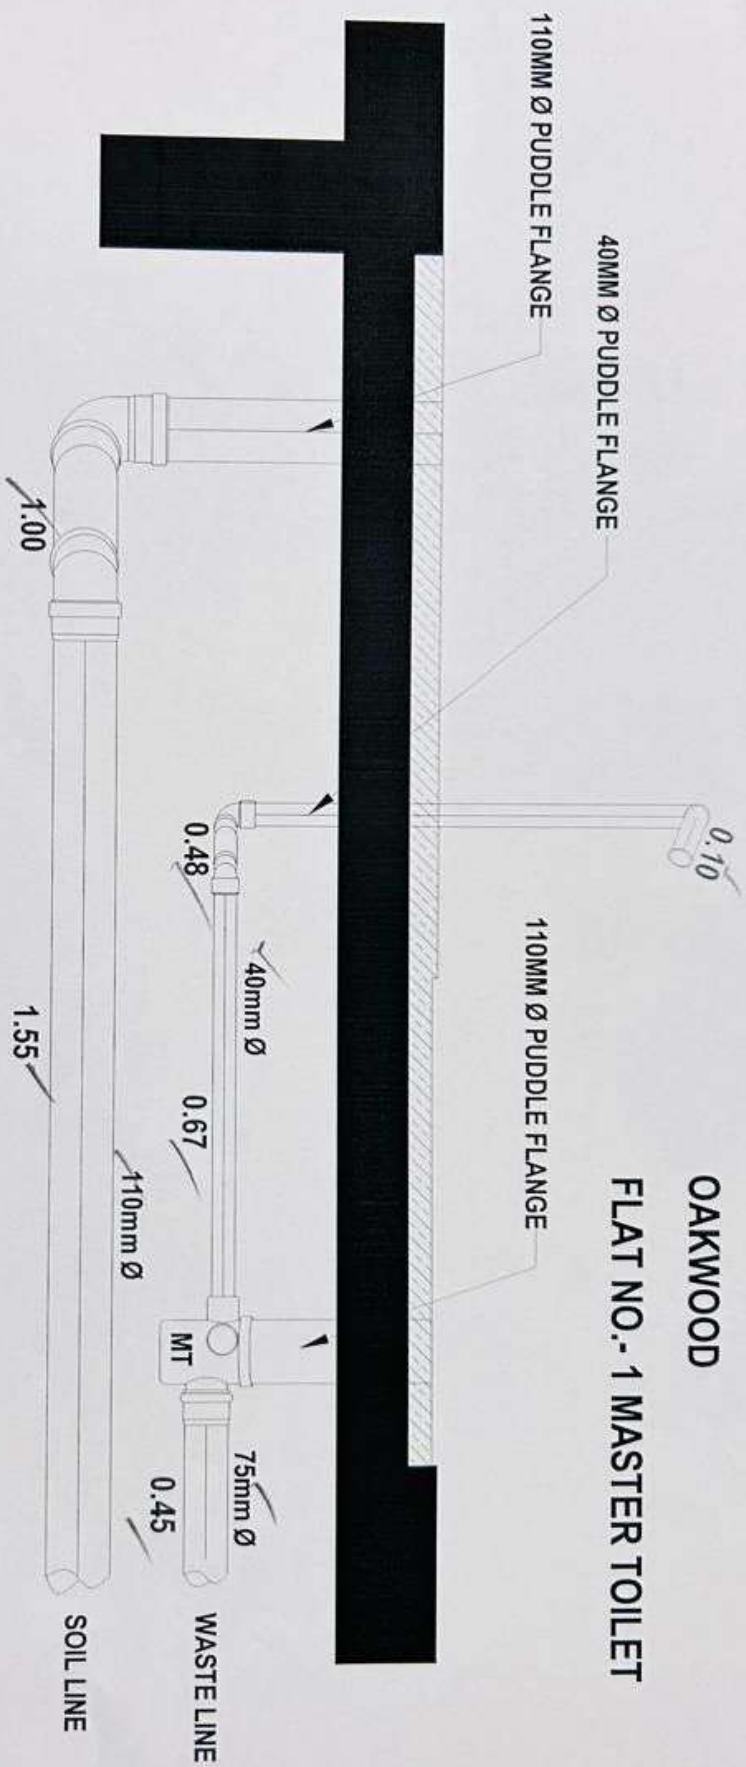

- 1- 110 MM Ø PVC SWR TYPE-B PIPE - 1.00+1.55 = 2.55 MTR. ✓
- 2- 75 MM Ø PVC SWR TYPE-B PIPE - 0.45 MTR. ✓
- 3- 40 MM Ø AGRI. 6KG. PIPE - 0.67+0.48+0.10 = 1.25 MTR. ✓
- 4- 110X75X50 MM Ø MULTI TRAP - 1 NO. ✓
- 5- 110X600 MM Ø PVC PUDDLE FLANGE - 2 NOS. ✓
- 6- 40X800 MM Ø PVC PUDDLE FLANGE - 1 NO. ✓


15

36/12/25



## OAKWOOD

### FLAT NO.- 1 COMMON TOILET

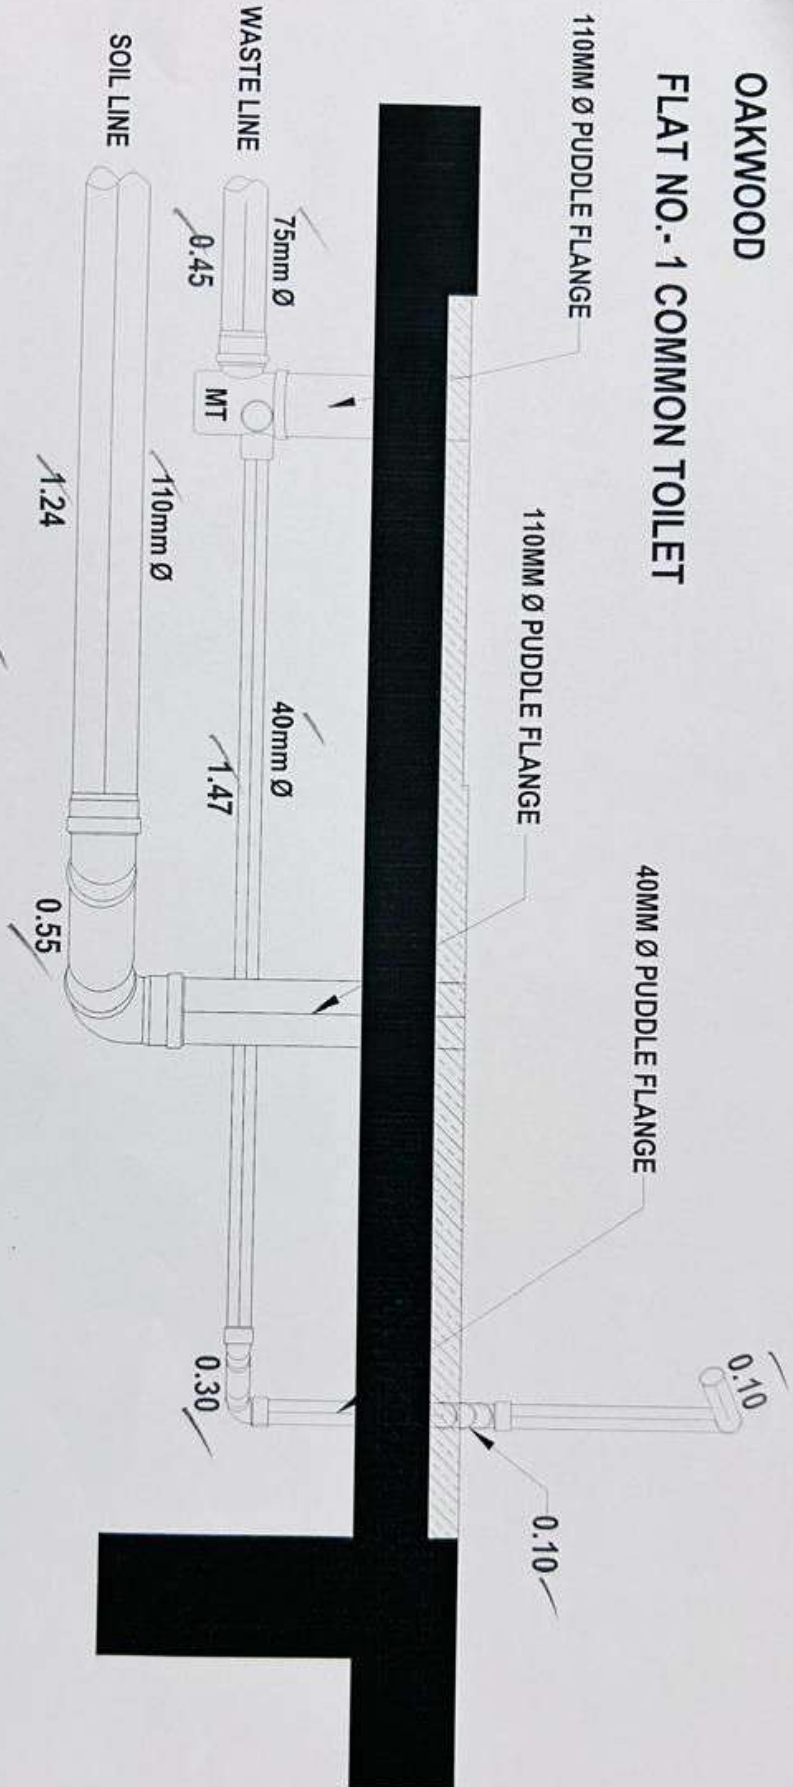


- 1- 110 MM Ø PVC SWR TYPE-B PIPE -  $1.24+0.55 = 1.79$  MTR.
- 2- 75 MM Ø PVC SWR TYPE-B PIPE - 0.45 MTR.
- 3- 40 MM Ø AGRI. 6KG. PIPE -  $1.47+0.30+0.10+0.10 = 1.97$  MTR.
- 4- 110X75X50 MM Ø MULTI TRAP - 1 NO.
- 5- 110X600 MM Ø PVC PUDDLE FLANGE - 2 NOS.
- 6- 40X800 MM Ø PVC PUDDLE FLANGE - 1 NO.

15/1

20/11/25



# OAKWOOD FLAT NO.- 1 KITCHEN

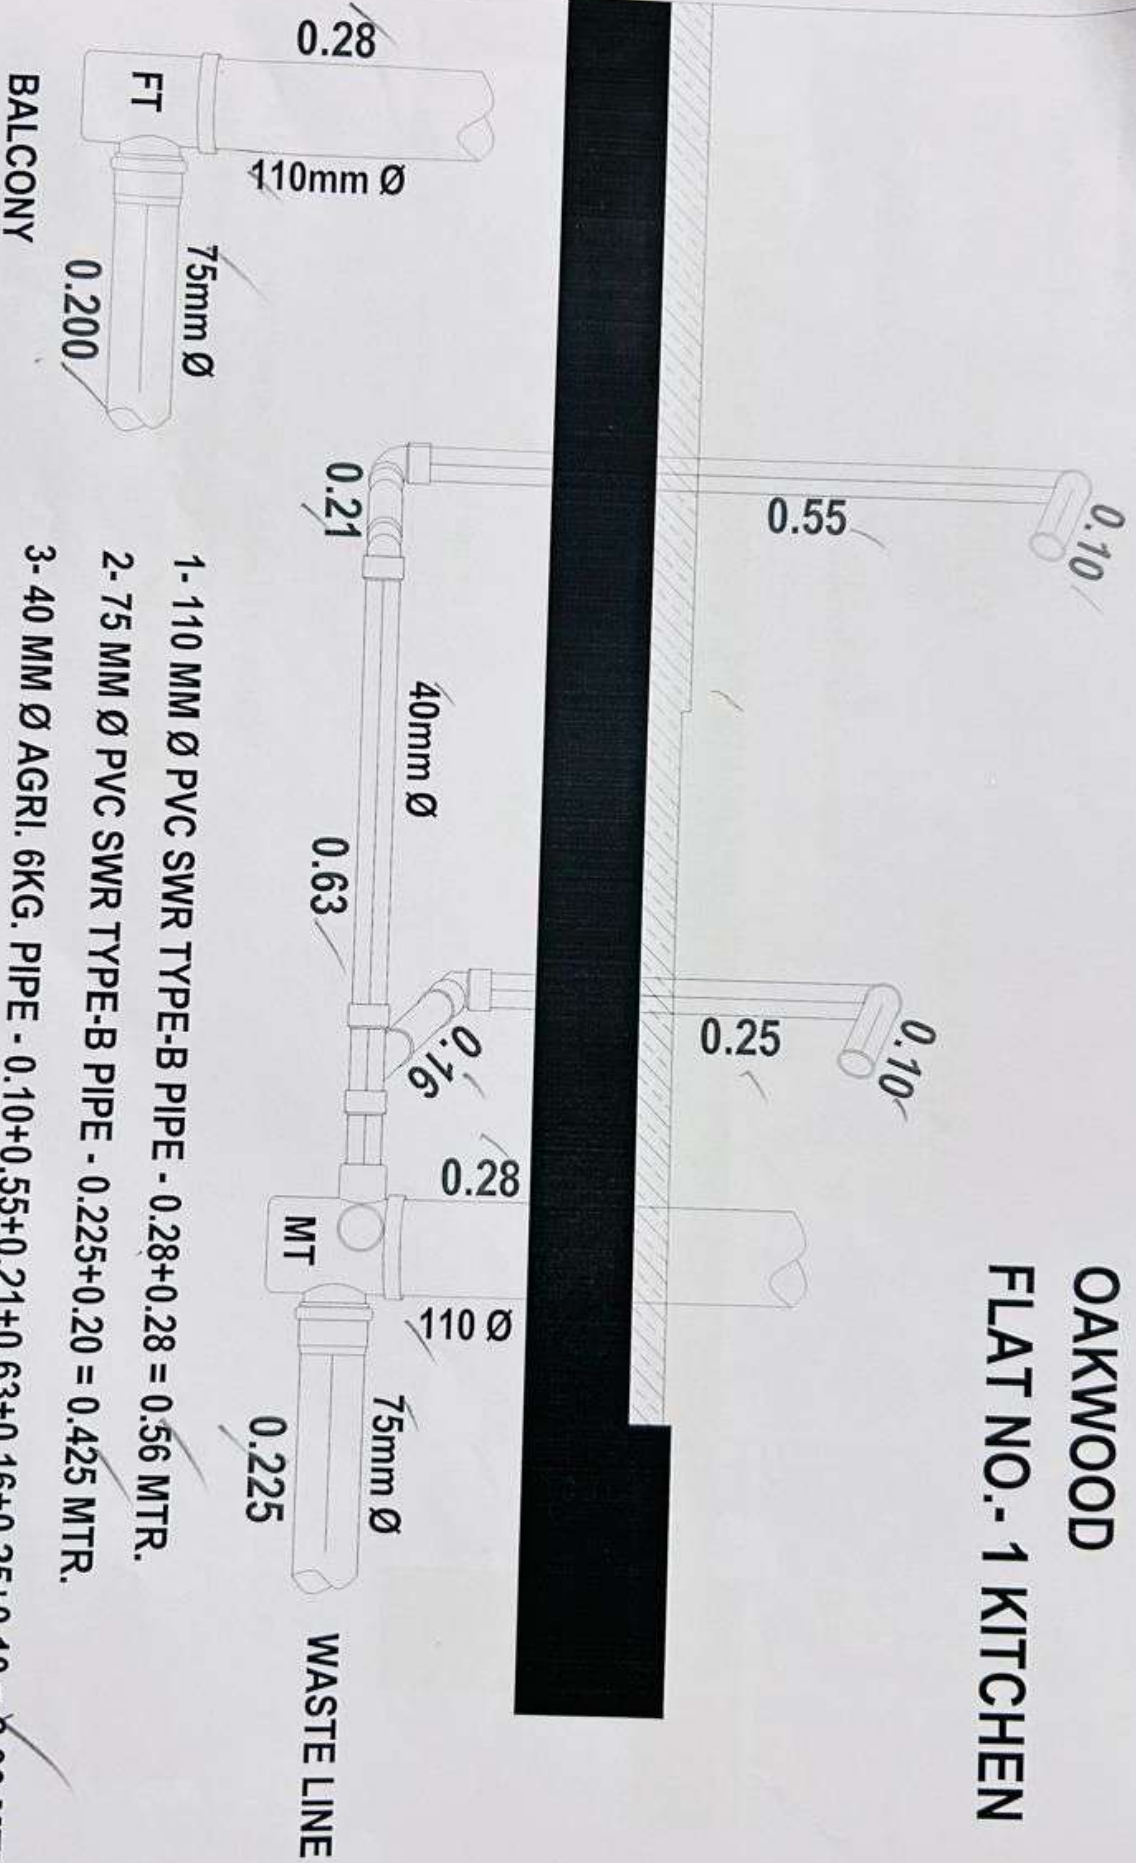

- 1- 110 MM Ø PVC SWR TYPE-B PIPE - 0.28+0.28 = 0.56 MTR.
- 2- 75 MM Ø PVC SWR TYPE-B PIPE - 0.225+0.20 = 0.425 MTR.
- 3- 40 MM Ø AGRI. 6KG. PIPE - 0.10+0.55+0.21+0.63+0.16+0.25+0.10 = 2.00 MTR.
- 4- 110X75X50 MM Ø MULTI TRAP - 1 NO.
- 5- 110X75 MM Ø FLOOR TRAP - 1 NO.

15/12/25

30/11/25